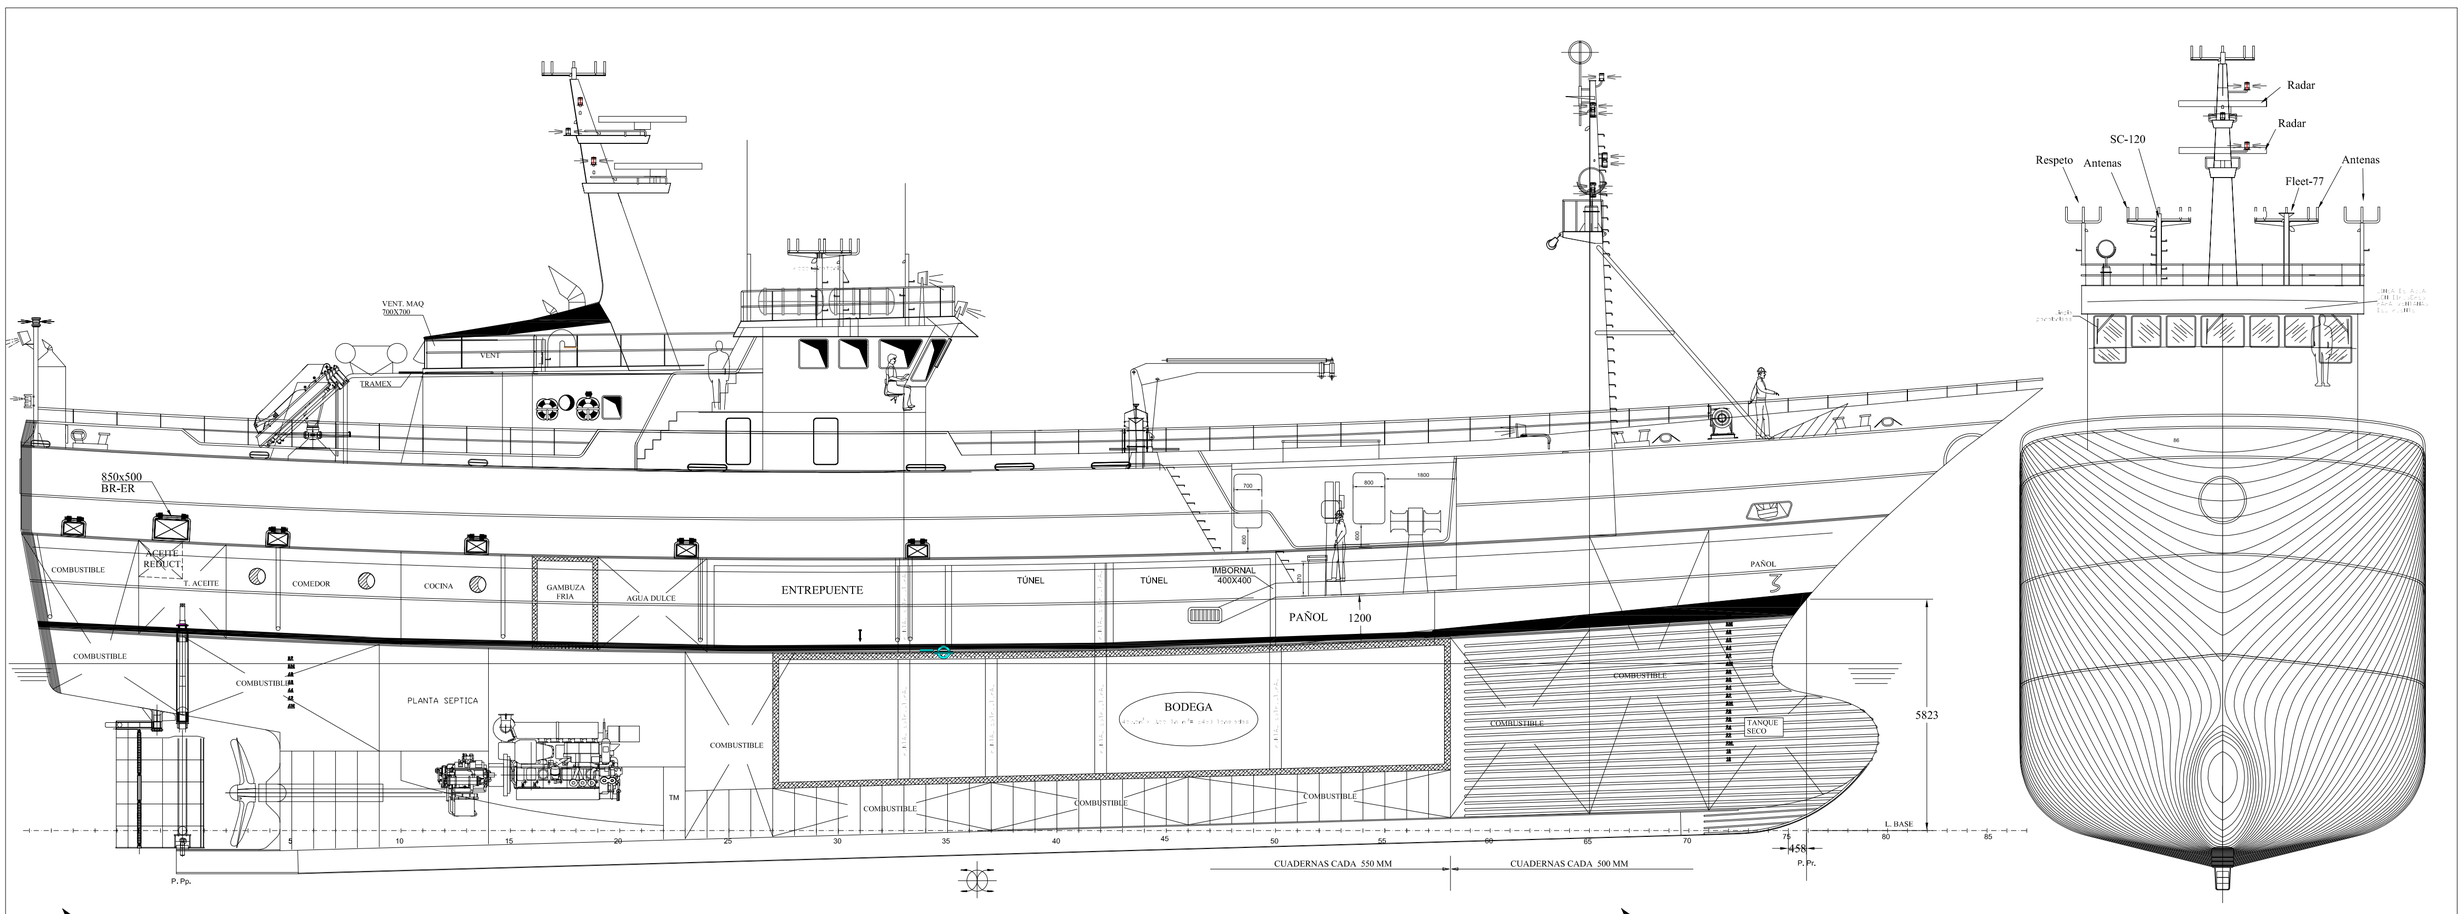

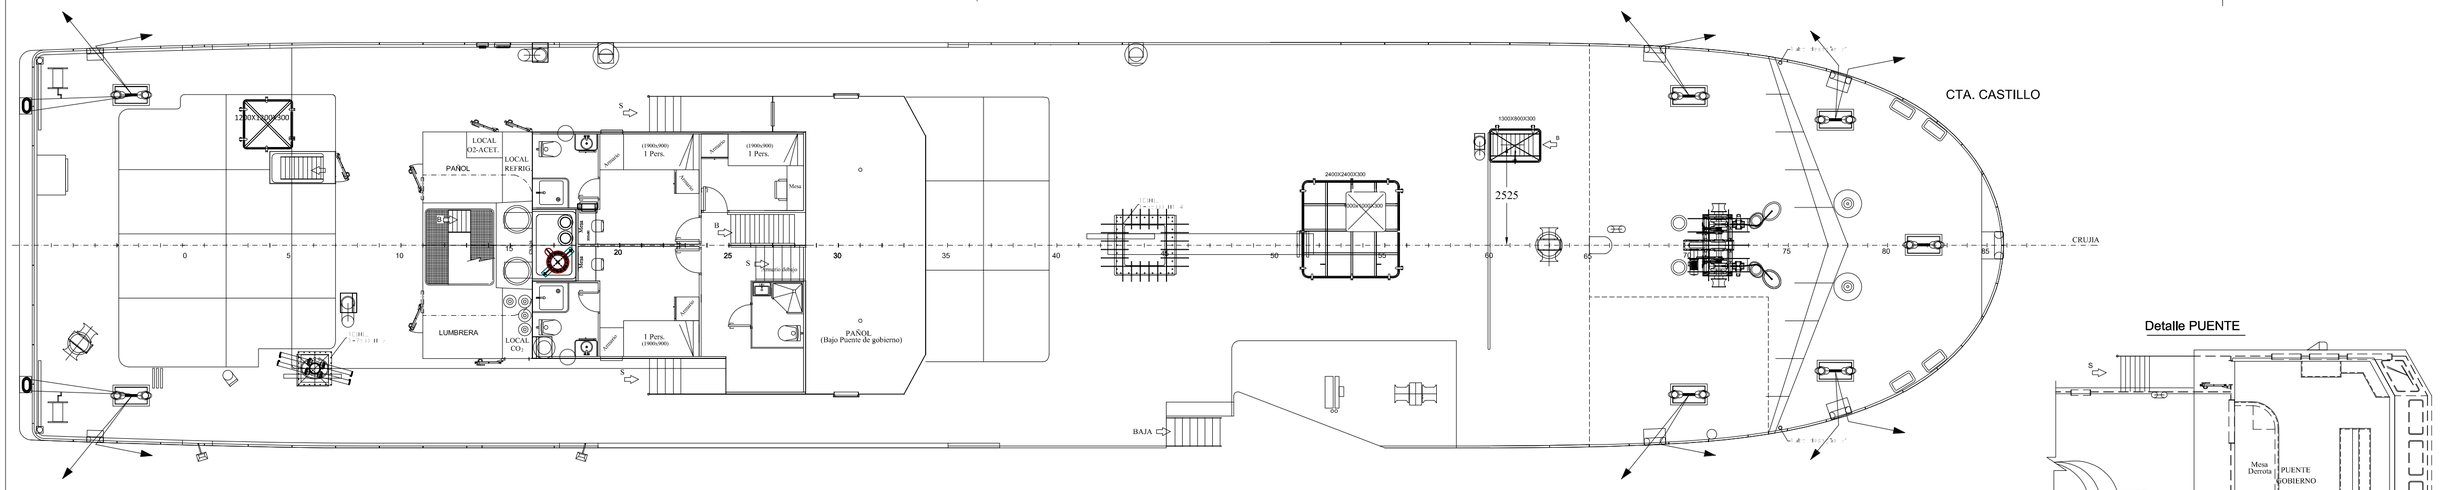

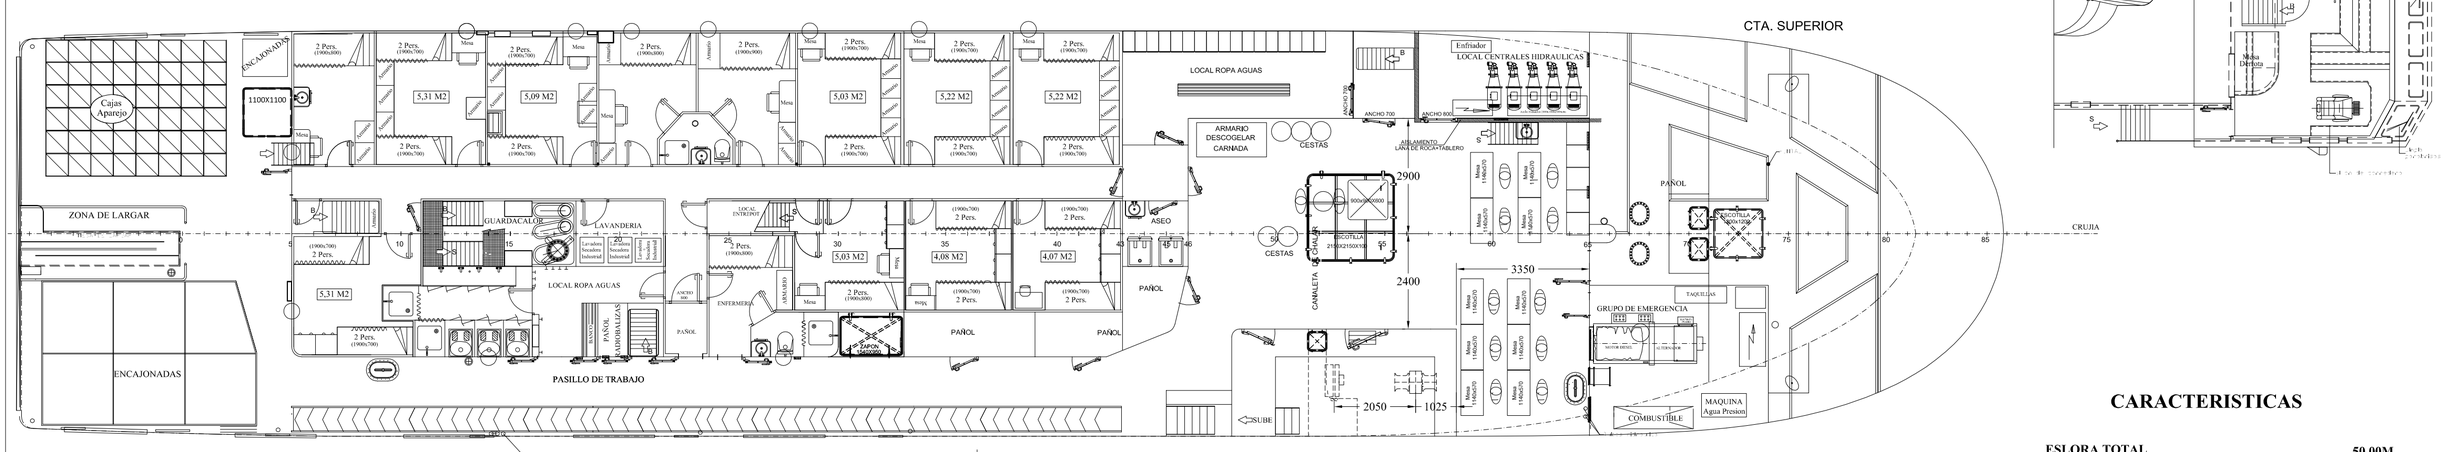

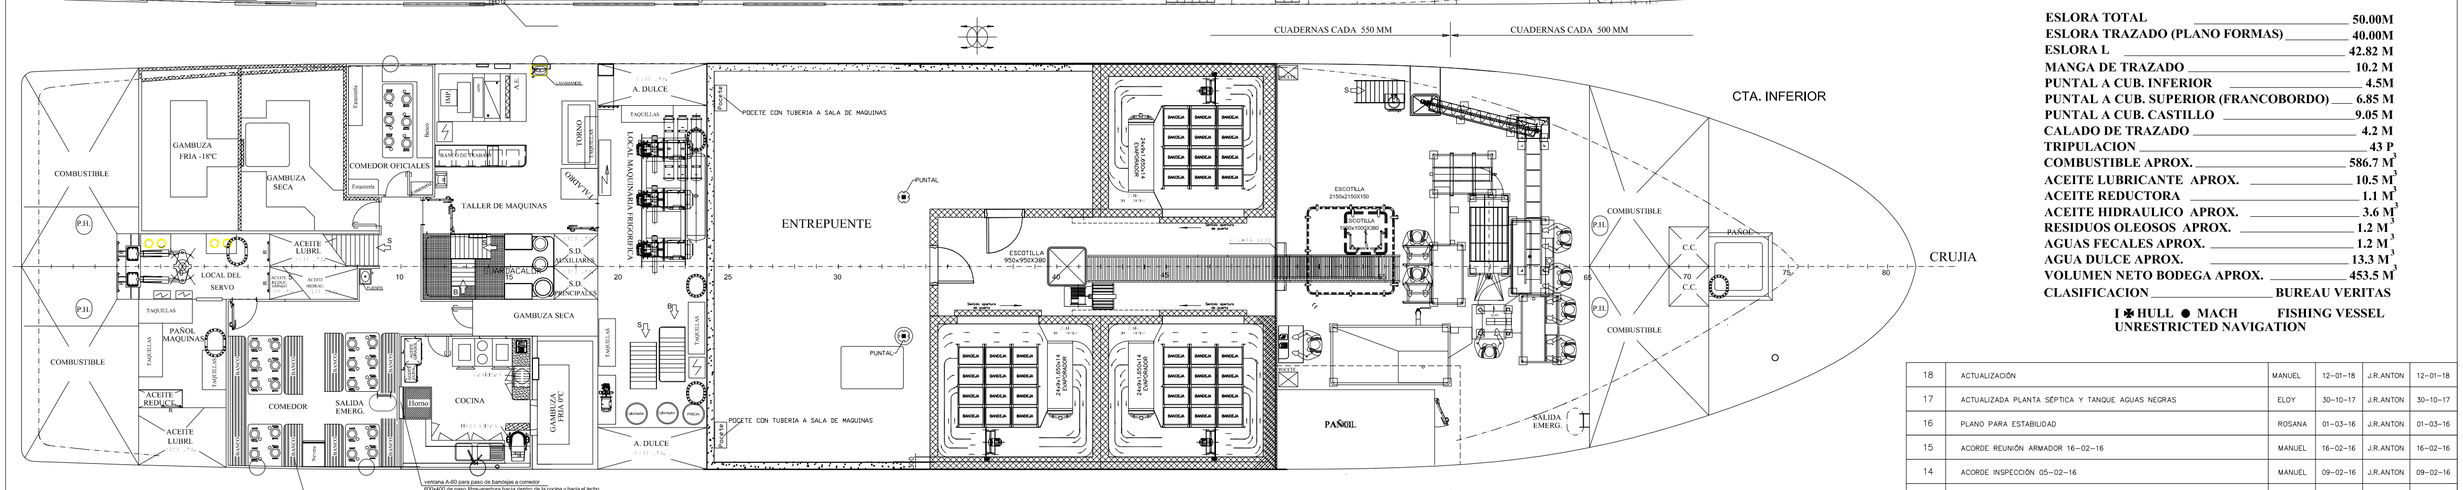

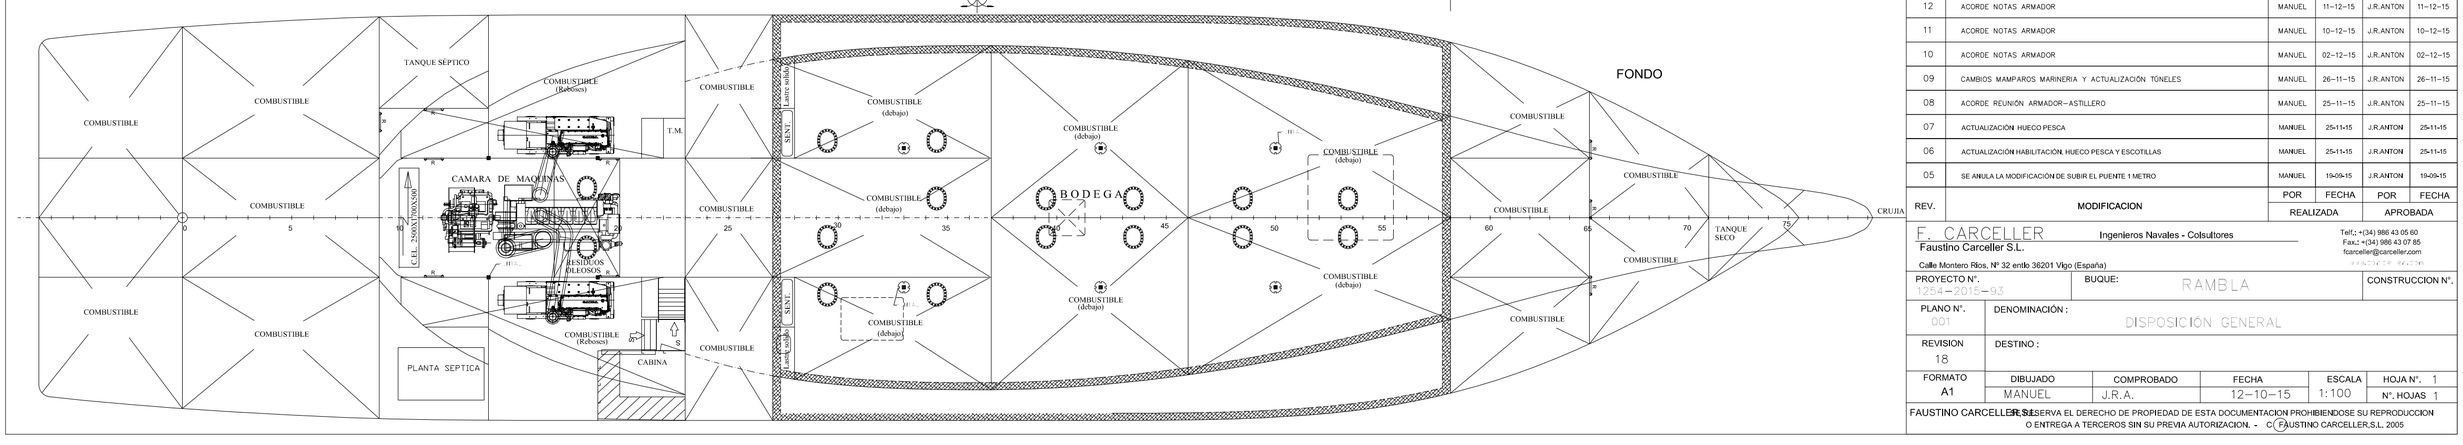

CARACTERISTICAS

ESLORA TOTAL	50.00M
ESLORA TRAZADO (PLANO FORMAS)	40.00M
ESLORA L	42.82 M
MANGA DE TRAZADO	10.2 M
PUNTAL A CUB. INFERIOR	4.5M
PUNTAL A CUB. SUPERIOR (FRANCOBORDO)	6.85 M
PUNTAL A CUB. CASTILLO	9.05 M
CALADO DE TRAZADO	4.2 M
TRIPULACION	43 P
COMBUSTIBLE APROX.	586.7 M^3
ACEITE LUBRICANTE APROX.	10.5 M^3
ACEITE REDUCTORA	1.1 M^3
ACEITE HIDRAULICO APROX.	3.6 M^3
RESIDUOS OLEOSOS APROX.	1.2 M^3
AGUAS FECALES APROX.	1.2 M^3
AGUA DULCE APROX.	13.3 M^3
VOLUMEN NETO BODEGA APROX.	453.5 M^3
CLASIFICACION	BUREAU VERITAS

I ✠ HULL ● MACH FISHING VESSEL
UNRESTRICTED NAVIGATION

REV.	MODIFICACION	POR	FECHA	POR	FECHA
		REALIZADA		APROBADA	
18	ACTUALIZACIÓN	MANUEL	12-01-18	J.R.ANTON	12-01-18
17	ACTUALIZADA PLANTA SÉPTICA Y TANQUE AGUAS NEGRAS	ELOY	30-10-17	J.R.ANTON	30-10-17
16	PLANO PARA ESTABILIDAD	ROSANA	01-03-16	J.R.ANTON	01-03-16
15	ACORDE REUNIÓN ARMADOR 16-02-16	MANUEL	16-02-16	J.R.ANTON	16-02-16
14	ACORDE INSPECCIÓN 05-02-16	MANUEL	09-02-16	J.R.ANTON	09-02-16
13	ACORDE NOTAS ARMADOR	MANUEL	18-01-16	J.R.ANTON	18-01-16
12	ACORDE NOTAS ARMADOR	MANUEL	11-12-15	J.R.ANTON	11-12-15
11	ACORDE NOTAS ARMADOR	MANUEL	10-12-15	J.R.ANTON	10-12-15
10	ACORDE NOTAS ARMADOR	MANUEL	02-12-15	J.R.ANTON	02-12-15
09	CAMBIOS MAMPAROS MARINERIA Y ACTUALIZACIÓN TÚNELES	MANUEL	26-11-15	J.R.ANTON	26-11-15
08	ACORDE REUNIÓN ARMADOR-ASTILLERO	MANUEL	25-11-15	J.R.ANTON	25-11-15
07	ACTUALIZACIÓN HUECO PESCA	MANUEL	25-11-15	J.R.ANTON	25-11-15
06	ACTUALIZACIÓN HABILITACIÓN HUECO PESCA Y ESCOTILLAS	MANUEL	25-11-15	J.R.ANTON	25-11-15
05	SE ANULA LA MODIFICACIÓN DE SUBIR EL PUENTE 1 METRO	MANUEL	19-09-15	J.R.ANTON	19-09-15

F. CARCELLER Ingenieros Navales - Colsultores
Faustino Carceller S.L.
Calle Montero Ríos, Nº 32 entlo 36201 Vigo (España)
Telf.: +(34) 986 43 05 60
Fax.: +(34) 986 43 07 85
fcarceller@carceller.com

PROYECTO Nº. 1254-2015-93	BUQUE: RAMBLA	CONSTRUCCION Nº.
PLANO Nº. 001	DENOMINACIÓN : DISPOSICIÓN GENERAL	
REVISION 18	DESTINO :	

FORMATO	DIBUJADO	COMPROBADO	FECHA	ESCALA	HOJA Nº. 1
A1	MANUEL	J.R.A.	12-10-15	1:100	Nº. HOJAS 1

FAUSTINO CARCELLER S.L. SE RESERVA EL DERECHO DE PROPIEDAD DE ESTA DOCUMENTACION PROHIBIENDOSE SU REPRODUCCION O ENTREGA A TERCEROS SIN SU PREVIA AUTORIZACION. - C (F) AUSTINO CARCELLER,S.L. 2005